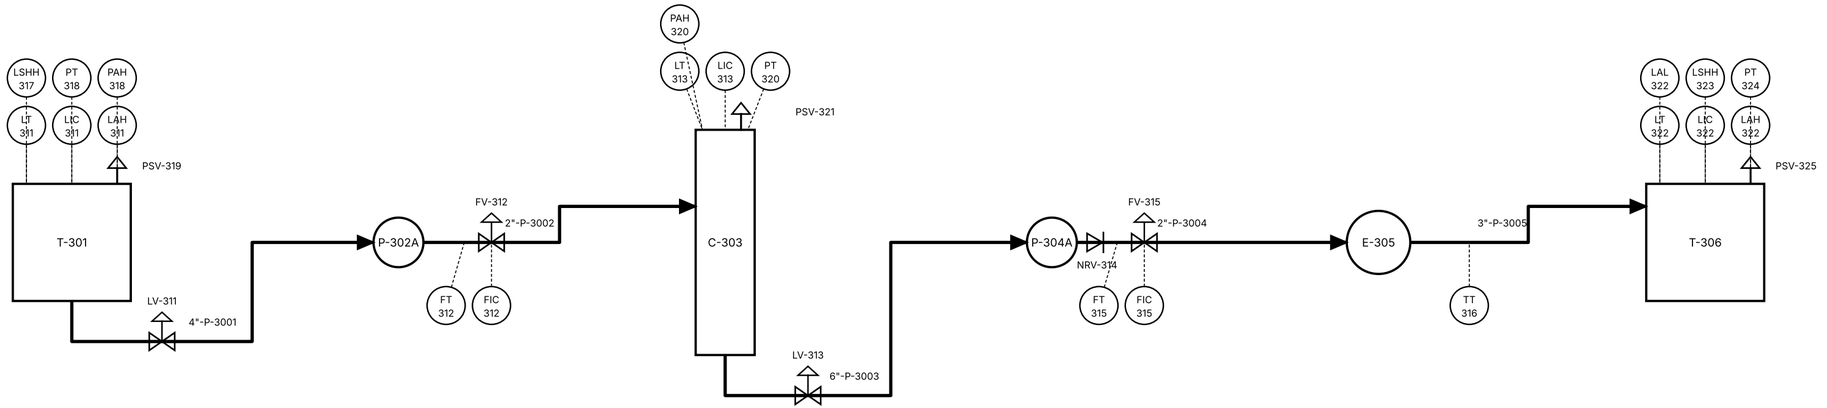

SYNTHETIC P&ID - NOT A REAL PLANT

DWG SYN-PID-028 UNIT 3

Generated for a portfolio demo