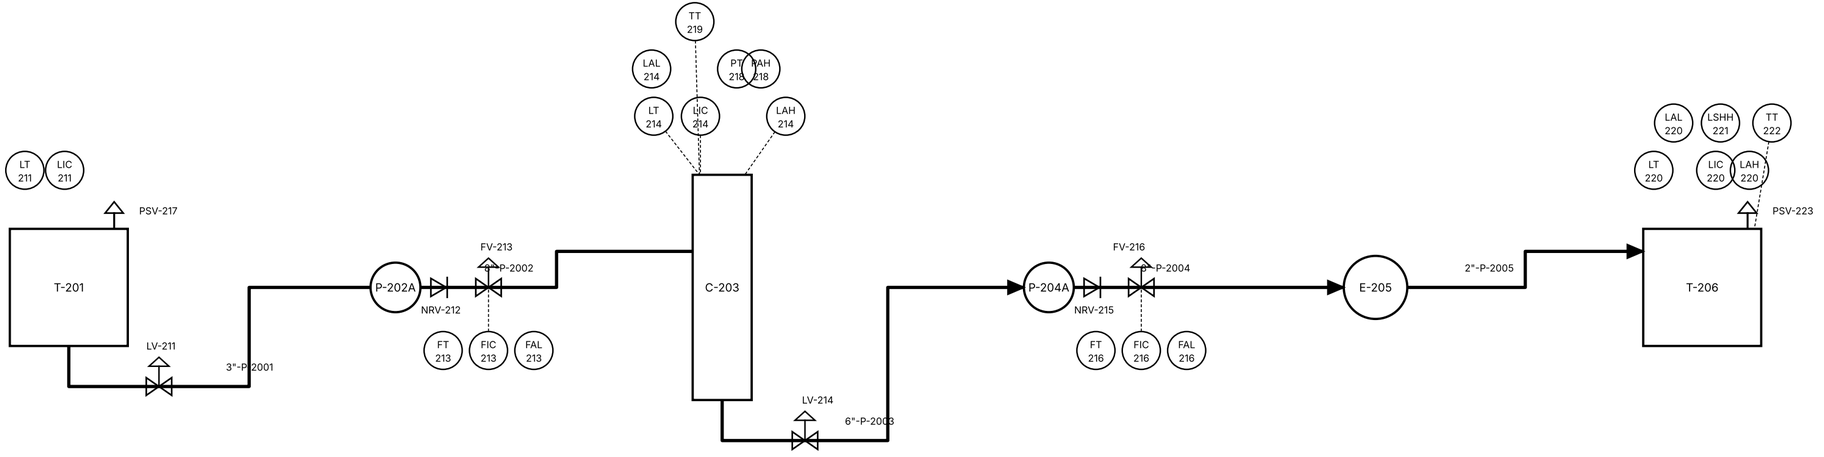

SYNTHETIC P&ID - NOT A REAL PLANT

DWG SYN-HARD-007 UNIT 2

Generated for a portfolio demo