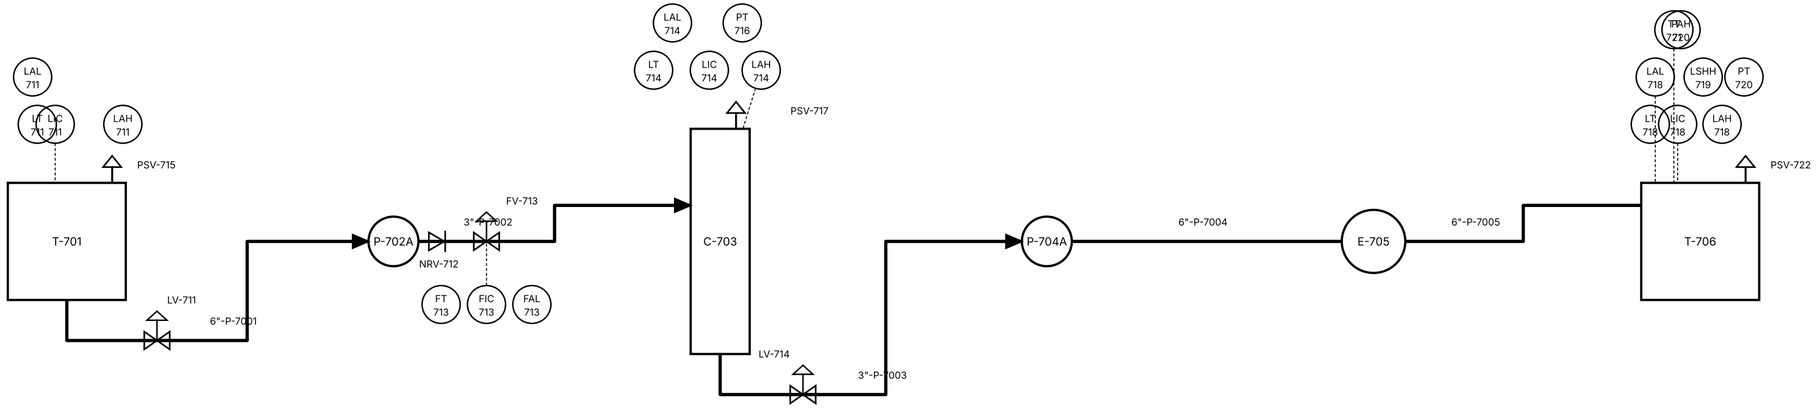

SYNTHETIC P&ID - NOT A REAL PLANT

DWG SYN-HARD-008 UNIT 7

Generated for a portfolio demo