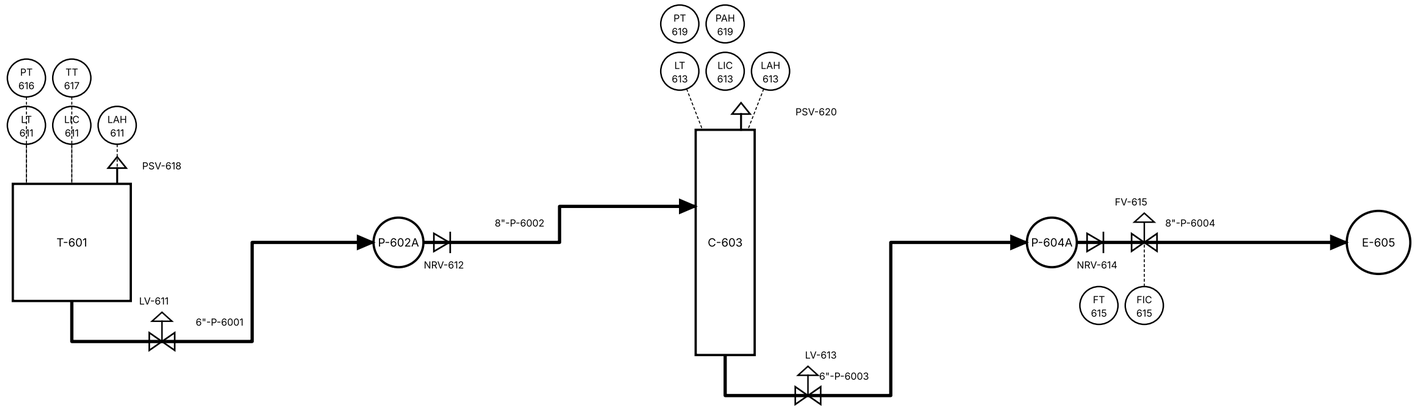

SYNTHETIC P&ID - NOT A REAL PLANT

DWG SYN-PID-026 UNIT 6

Generated for a portfolio demo